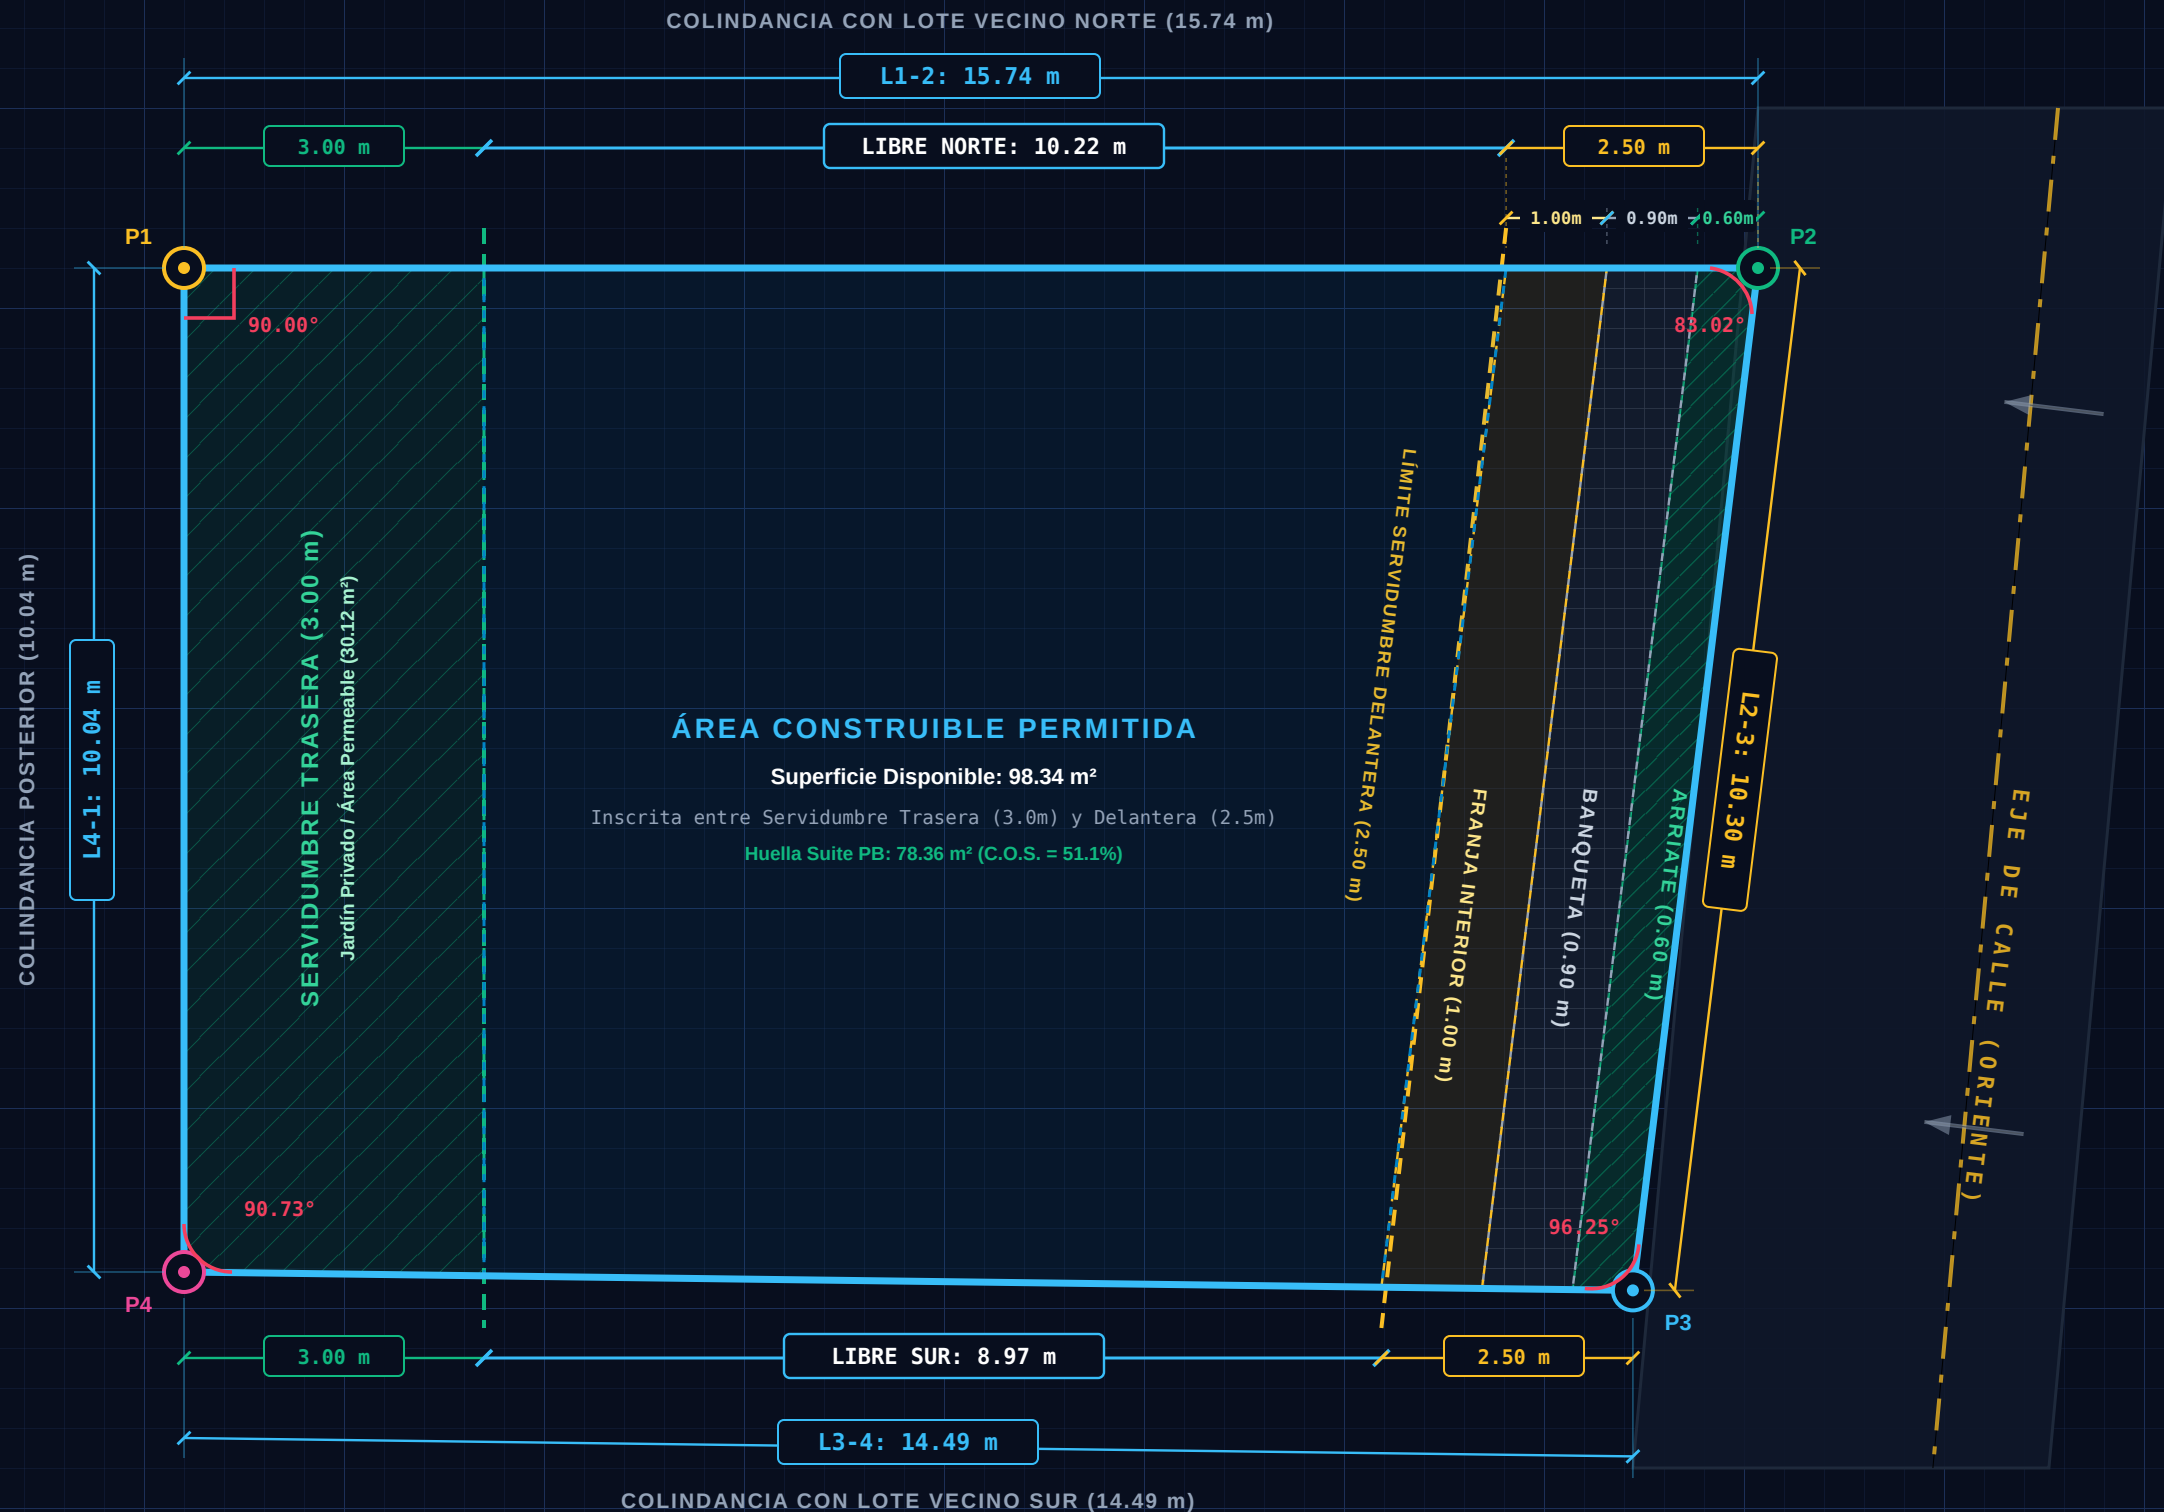


CUADRO DE CONSTRUCCIÓN (COORDENADAS EXACTAS)

EST	P.V.	RUMBO	DISTANCIA	COORD X (m)	COORD Y (m)
P1	P2	N 90°00'00" E	15.740 m	0.000	0.000
P2	P3	S 06°58'34" W	10.300 m	15.740	0.000
P3	P4	S 89°16'05" W	14.489 m	14.489	-10.224
P4	P1	N 00°00'00" E	10.040 m	0.000	-10.040
SUPERFICIE TOTAL:		153.19 m²	PERÍMETRO:	50.57 m	
ESQUINA RECTA:		P1 = 90.00° (Nor-Poniente)		DIAGONAL FRENTE:	ΔX = -1.25 m (6.98°)

DESGLOSE DE SERVIDUMBRES Y DIMENSIONES LIBRES

CONCEPTO	DIMENSIÓN	SUPERFICIE
Servidumbre Trasera (Jardín)	3.00 m fondo	30.12 m²
Servidumbre Delantera Total	2.50 m (oblicua)	24.73 m²
↳ Arriate ajardinado (frente)	0.60 m	6.18 m²
↳ Banqueta peatonal	0.90 m	9.27 m²
↳ Franja interior de servidumbre	1.00 m	9.28 m²
Longitud Libre Construible Norte	10.22 m	(15.74 - 3.0 - 2.52)
Longitud Libre Construible Sur	8.97 m	(14.49 - 3.0 - 2.52)
SUPERFICIE CONSTRUIBLE TOTAL	8.97m a 10.22m	98.34 m²

CASA 235 • PLANO TOPOGRÁFICO Y SERVIDUMBRES

PROYECTO:
Levantamiento Geométrico, Servidumbres y Cotas Libres

UBICACIÓN:
Tlajomulco de Zúñiga, Jalisco

VIALIDAD:
Oriente / Este (Alineamiento L2-3)

SUPERFICIE:
153.19 m²

PERÍMETRO:
50.57 m

USO DE SUELO:
Habitacional (H3/H4)

ESCALA: 1:50 / Gráfica

ACOTACIONES: Metros (m)

FECHA: Septiembre 2026

CLAVE: TOP-01

SISTEMA: Cartesiano Ortogonal • Origen P1 (90.00°) • Servidumbre Frontal 2.50m (Arriate 0.6m + Banqueta 0.9m + 1.0m) • Inkscape 1.4

ESCALA GRÁFICA (METROS)

