


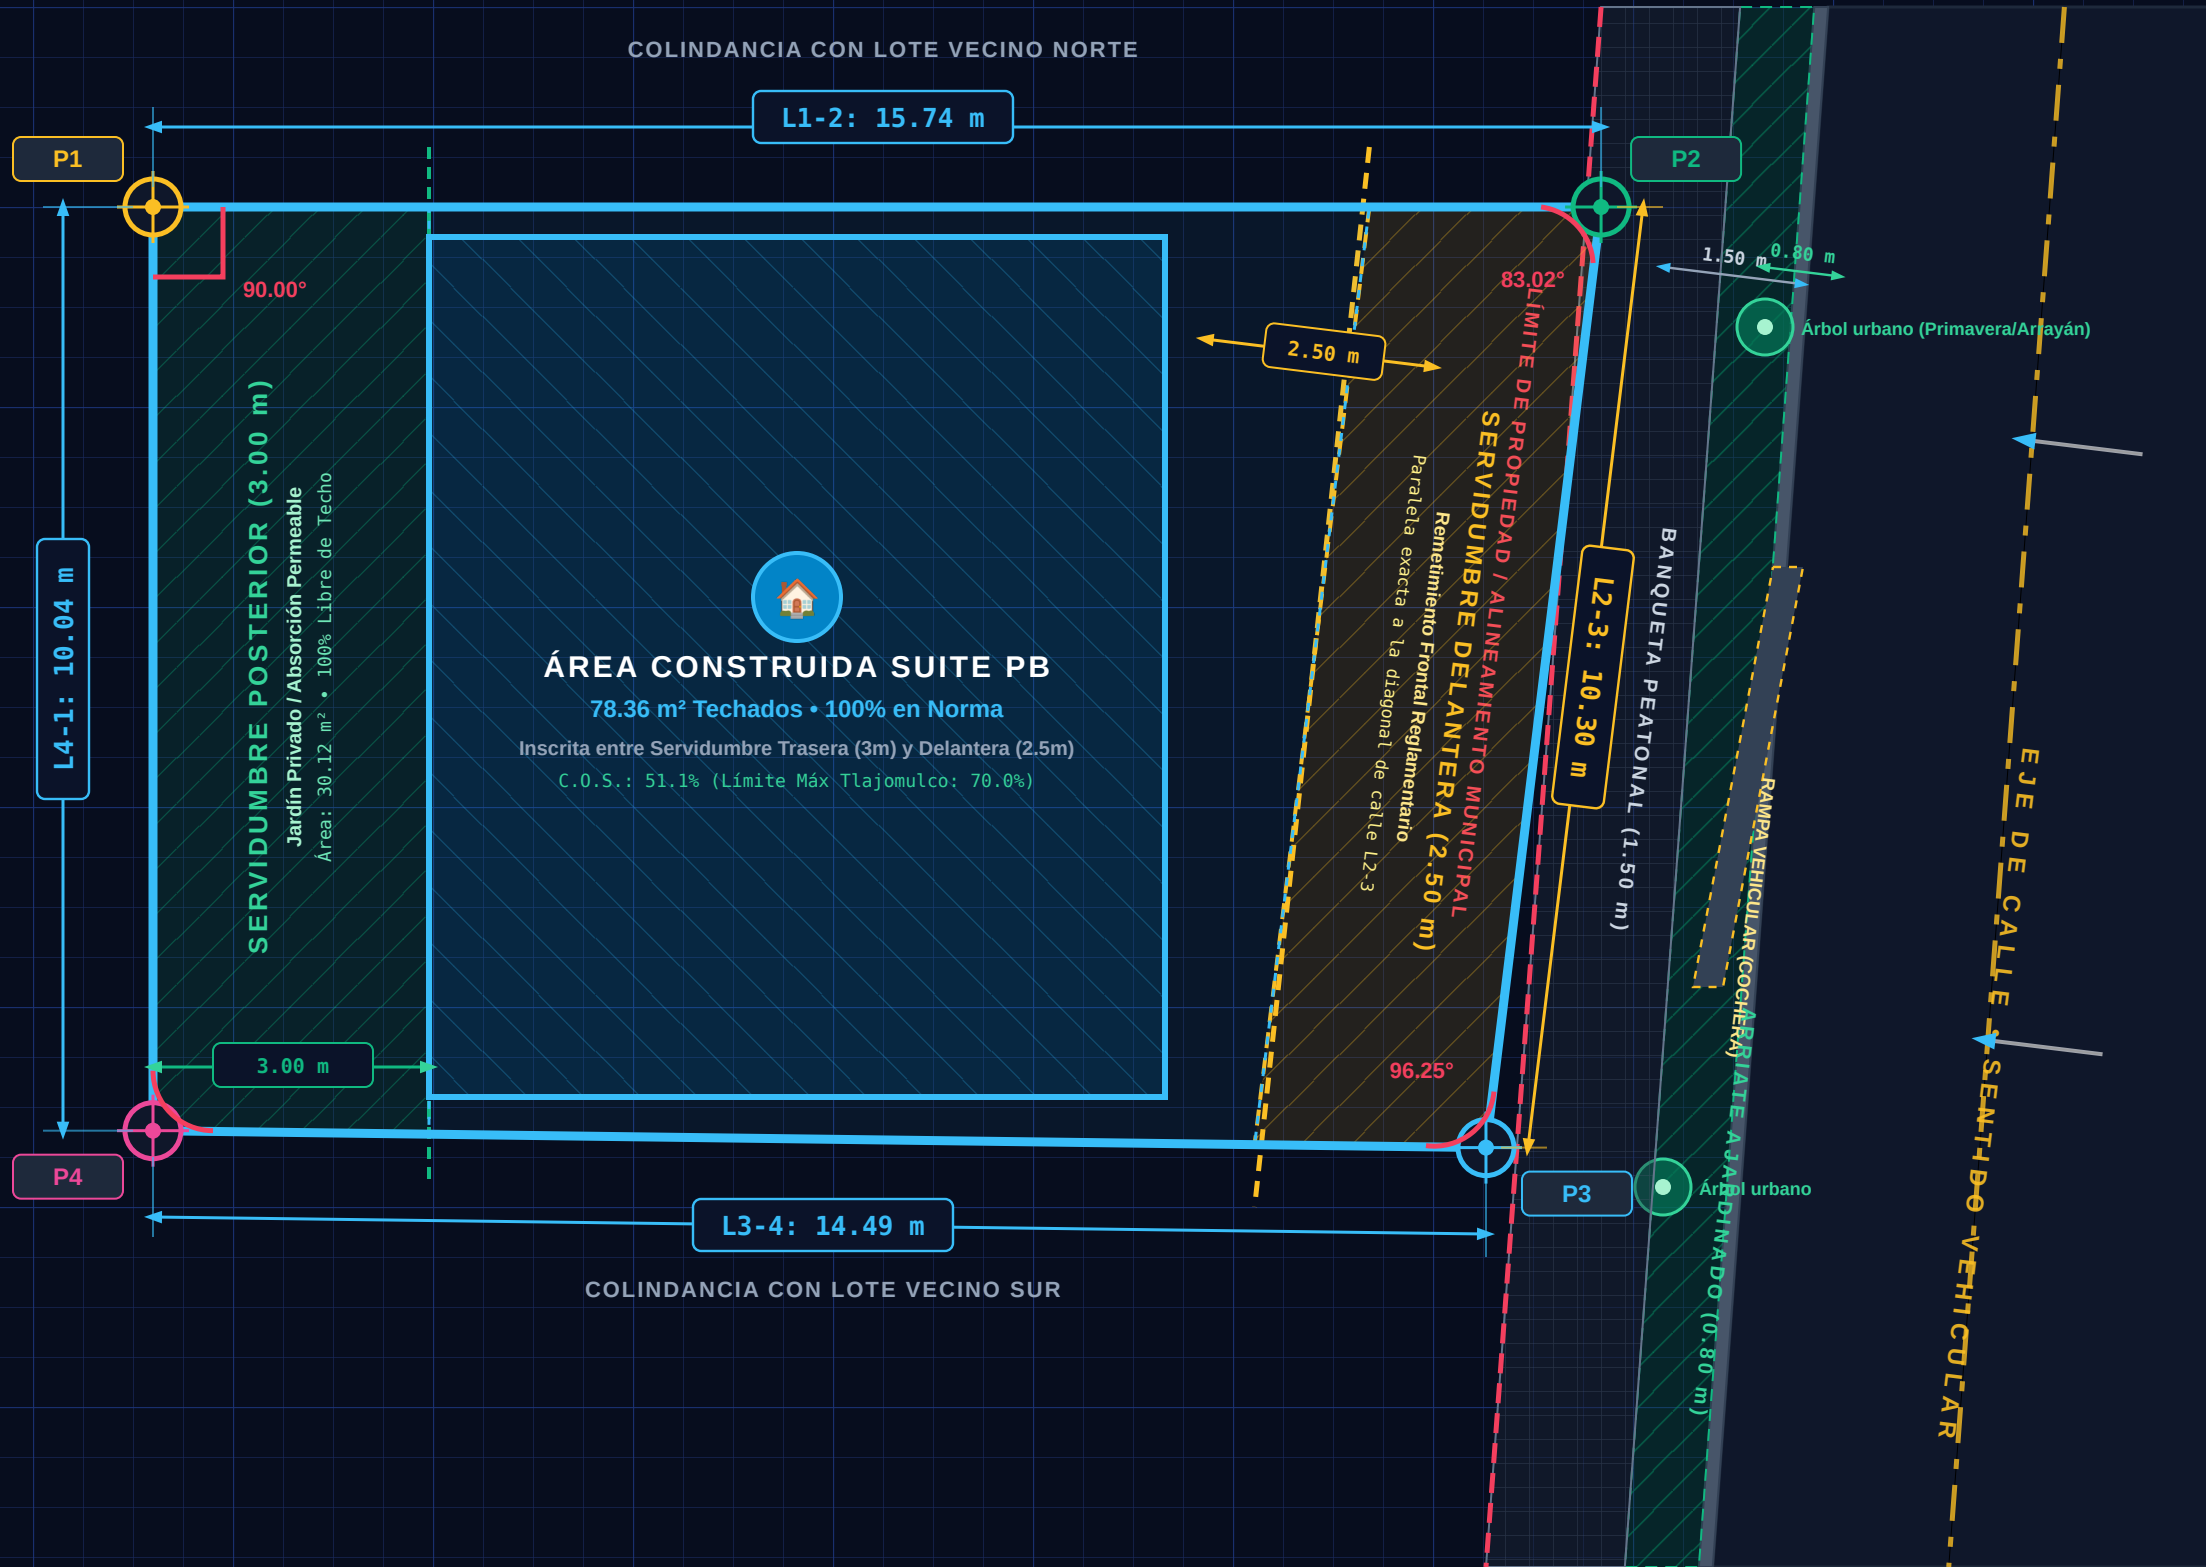

CUADRO OFICIAL DE CONSTRUCCIÓN (COORDENADAS CARTESIANAS)					
EST	P.V.	RUMBO	DISTANCIA	COORD X (m)	COORD Y (m)
P1	P2	N 90°00'00" E	15.740 m	0.000 m	0.000 m
P2	P3	S 06°58'34" W	10.300 m	15.740 m	0.000 m
P3	P4	S 89°16'05" W	14.489 m	14.489 m	-10.224 m
P4	P1	N 00°00'00" E	10.040 m	0.000 m	-10.040 m
SUPERFICIE:		153.19 m²	PERÍMETRO:	50.57 m	
VÉRTICE RECTO:		P1 = 90.00° (Nor-Poniente)	DESVÍO CALLE:	ΔX = -1.25 m (6.98° al Este)	

SERVIDUMBRES Y PARÁMETROS URBANÍSTICOS (TLAJOMULCO H3/H4)			
CONCEPTO	REGLAMENTO	PROYECTO CASA 235	ESTATUS
Servidumbre Delantera	Mín. 2.50 m	2.50 m (Siguiendo diagonal L2-3)	EXACTA
Servidumbre Trasera	Mín. 3.00 m / 20%	3.00 m (Jardín 30.12 m²)	✓ CUMPLE
Sección Vial Exterior	Banqueta + Arriate	1.50 m Banq. + 0.80 m Arriate	✓ CUMPLE
C.O.S. (Ocupación PB)	Máx. 70.0% (107.2 m²)	51.1% (78.36 m² PB)	✓ CUMPLE
C.U.S. (Utilización)	Máx. 2.10 (321.7 m²)	0.51 (Fase 1 PB)	✓ CUMPLE
Área Libre Permeable	Mín. 25.0% (38.3 m²)	48.9% (74.83 m²)	✓ CUMPLE
⚠ REGLA CONSTRUCTIVA EN SERVIDUMBRE DELANTERA (2.50 m): El área de 2.50 m al frente sigue la diagonal L2-3. Prohibido construir muros cerrados o losas permanentes; se destina a rodamiento de cochera abierta y huella verde. La servidumbre trasera (3.00 m) garantiza absorción pluvial y ventilación de la Suite PB.			

CASA 235 • RESIDENCIA INTELIGENTE SICO-235 CAD

PLANO:
LEVANTAMIENTO TOPOGRÁFICO, SERVIDUMBRES Y SECCIÓN VIAL

UBICACIÓN:
Tlajomulco de Zúñiga, Jalisco

VIALIDAD:
Oriente / Este (Alineamiento)

SUPERFICIE:
153.19 m²

ESCALA: 1:50 / Gráfica ACOTACIONES: Metros (m) FECHA: Septiembre 2026 CLAVE: TOP-01

SISTEMA: Cartesiano Ortogonal • Origen P1 (90.00°) • Servidumbre Delantera 2.50m oblicua • Inkscape 1.4