
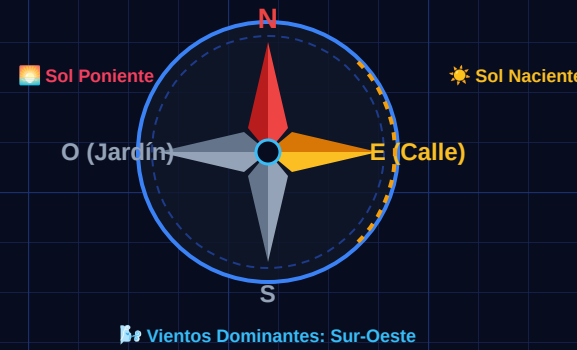


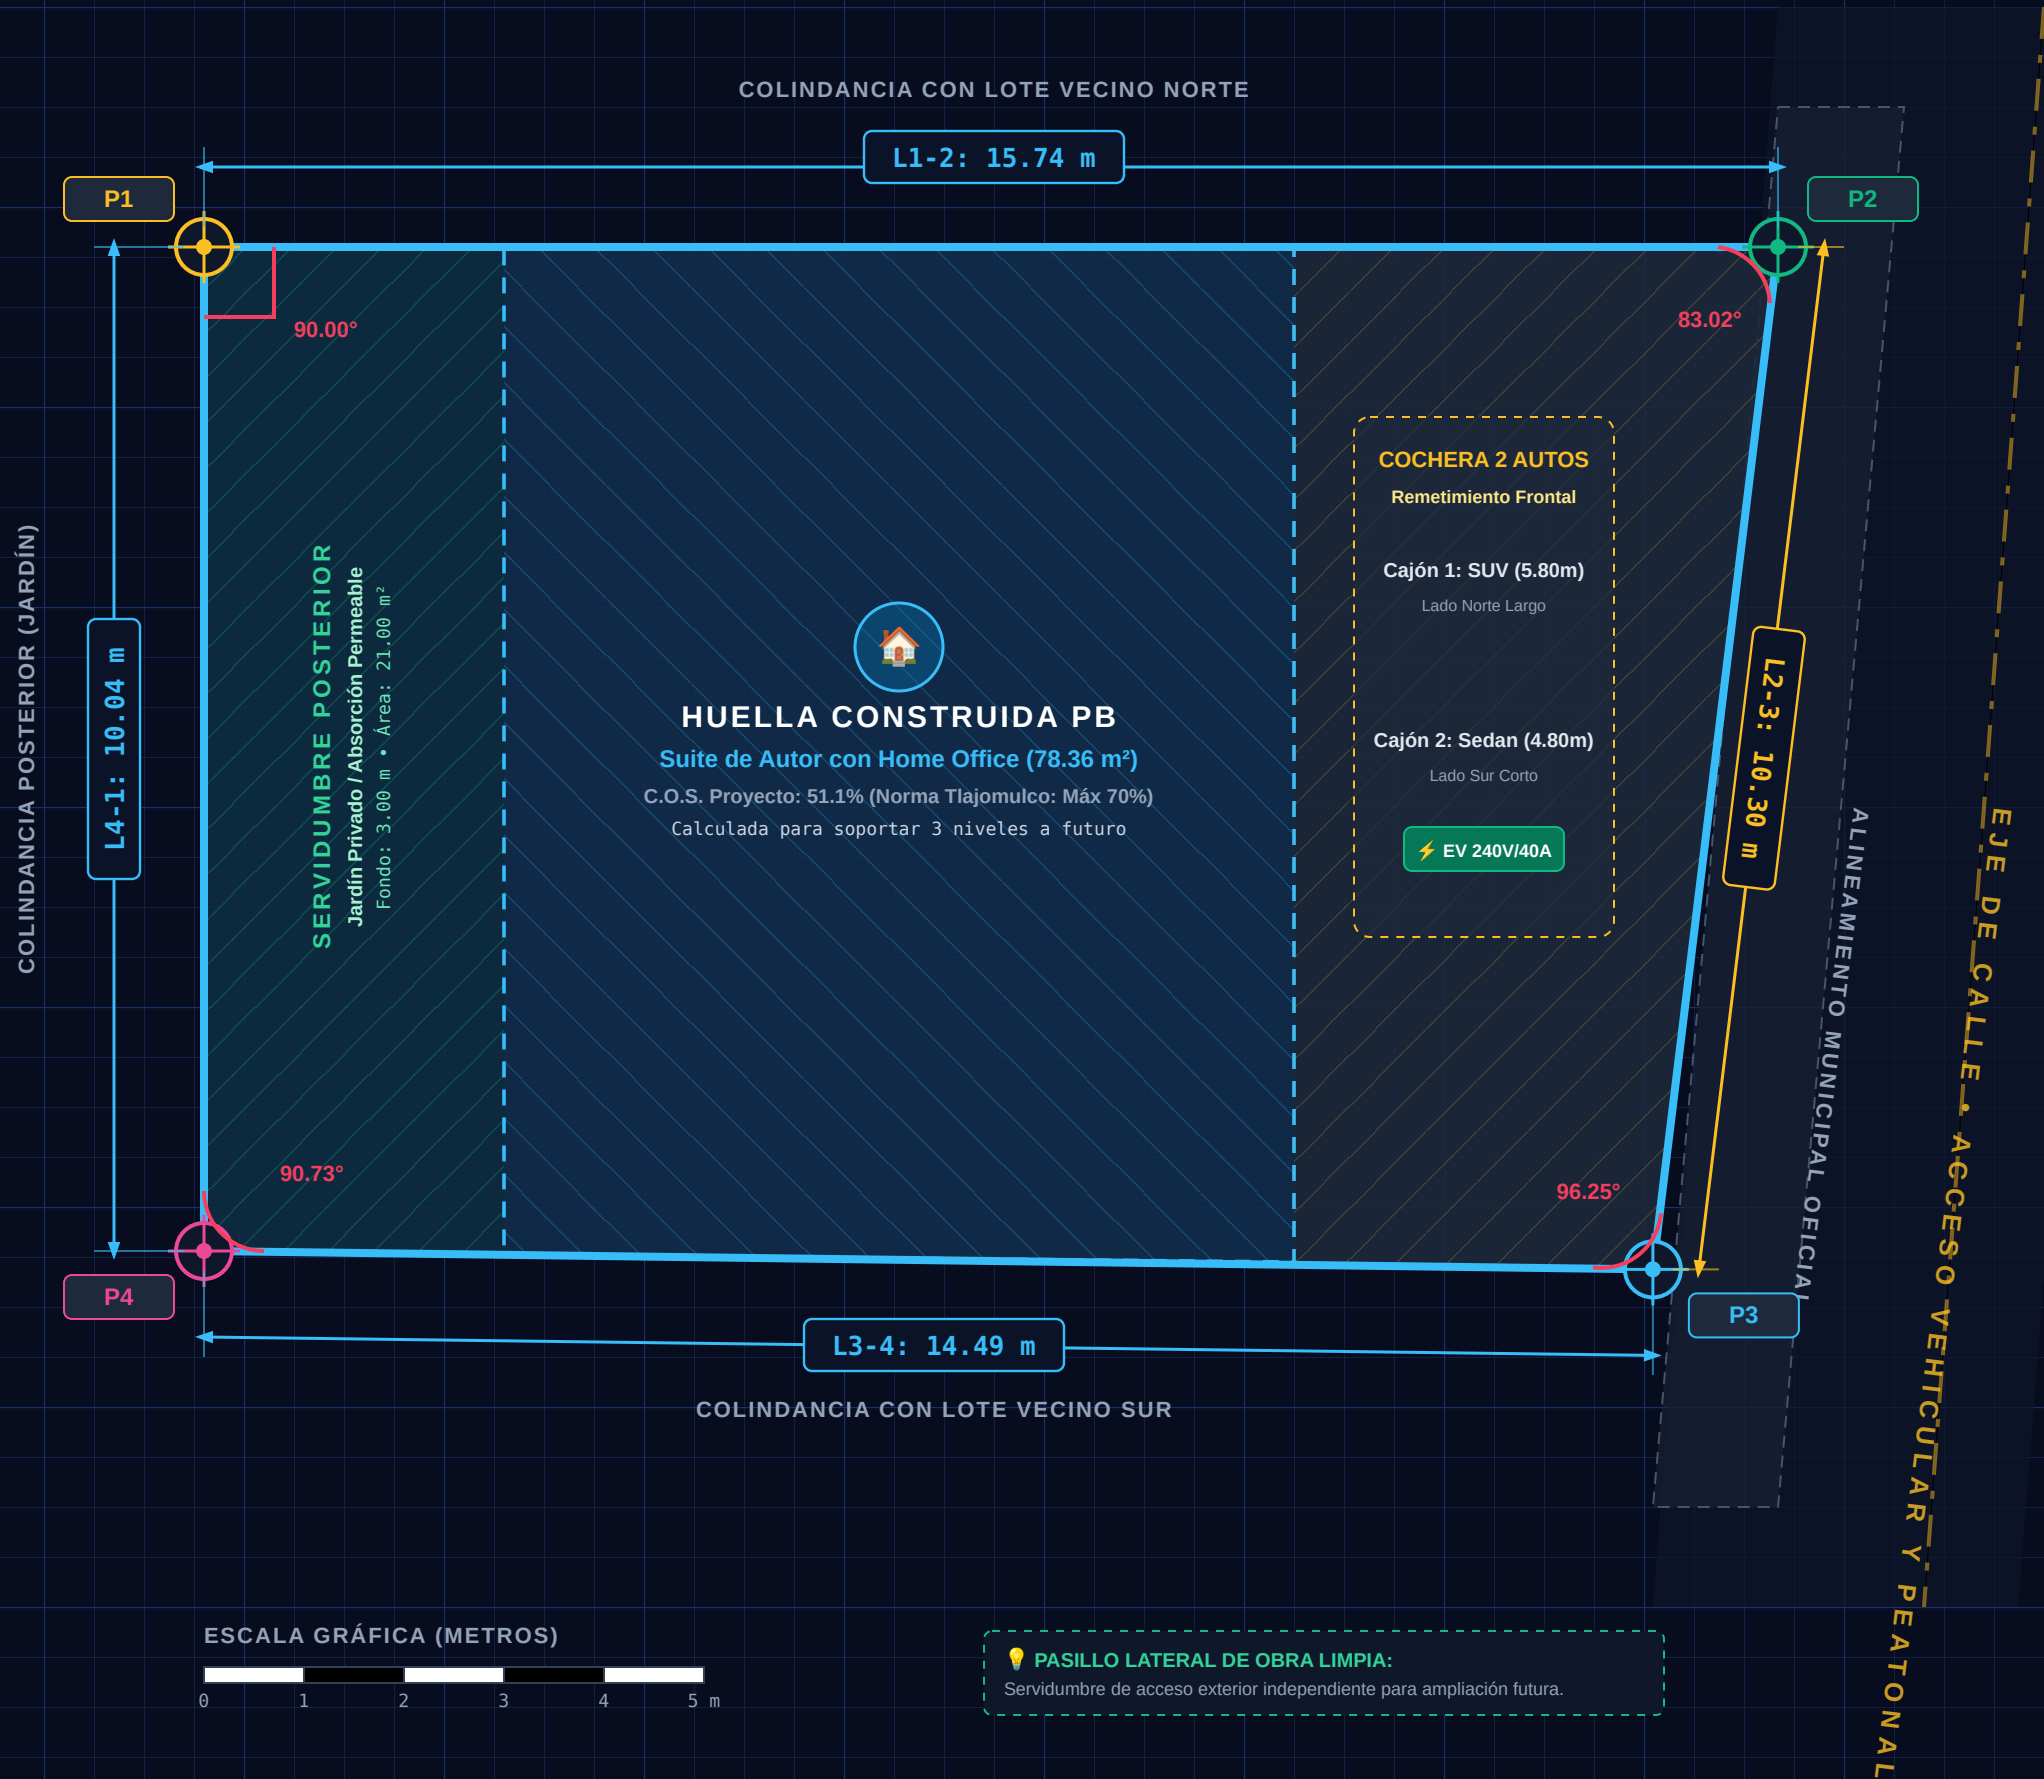

CUADRO OFICIAL DE CONSTRUCCIÓN (COORDENADAS CARTESIANAS)

EST	P.V.	RUMBO	DISTANCIA	COORD X (m)	COORD Y (m)
P1	P2	N 90°00'00" E	15.740 m	0.000 m	0.000 m
P2	P3	S 06°58'34" W	10.300 m	15.740 m	0.000 m
P3	P4	S 89°16'05" W	14.489 m	14.489 m	-10.224 m
P4	P1	N 00°00'00" E	10.040 m	0.000 m	-10.040 m

SUPERFICIE: 153.19 m² **PERÍMETRO:** 50.57 m

VÉRTICE RECTO: P1 = 90.00° Exacto (Origen 0,0) **DESVÍO CALLE:** ΔX = -1.25 m (6.98°)

PARÁMETROS URBANÍSTICOS Y RESTRICCIONES (TLAJOMULCO H3/H4)

CONCEPTO NORMATIVO	LÍMITE REGLAMENTARIO	PROYECTO CASA 235	ESTATUS
C.O.S. (Ocupación PB)	Máx. 70.0% (107.2 m²)	51.1% (78.36 m²)	✓ CUMPLE
C.U.S. (Utilización Total)	Máx. 2.10 (321.7 m²)	0.51 (Fase 1 PB)	✓ CUMPLE
Área Libre / Jardín	Mín. 25.0% (38.3 m²)	48.9% (74.83 m²)	✓ CUMPLE
Servidumbre Frontal	Mín. 1.50 m	4.75 m a 6.00 m	✓ CUMPLE
Altura Máxima	Máx. 3 Niveles (10.50m)	1 Nivel (3.15 m PB)	✓ CUMPLE

⚠️ NOTA MECÁNICA DE SUELOS (TLAJOMULCO):

Zona con presencia de arcillas expansivas (vertisoles). Se exige mejoramiento de suelo con banco de tepetate compactado y desplante de zapatas a estrato firme certificado.

CASA 235 • RESIDENCIA INTELIGENTE

SICO-235 CAD

PLANO: LEVANTAMIENTO TOPOGRÁFICO, COLINDANCIAS Y RESTRICCIONES

UBICACIÓN: Tlajomulco de Zúñiga, Jalisco (ZMG) **USO DE SUELO:** Habitacional Unifamiliar (H3/H4) **SUPERFICIE:** 153.19 m²

ESCALA: 1:50 / Gráfica **ACOTACIONES:** Metros (m) **FECHA:** Septiembre 2026 **CLAVE:** TOP-01

SISTEMA: Coordenadas Cartesiano Ortogonal • Origen P1 (90.00°) • Software: Inkscape 1.4 Vectorial