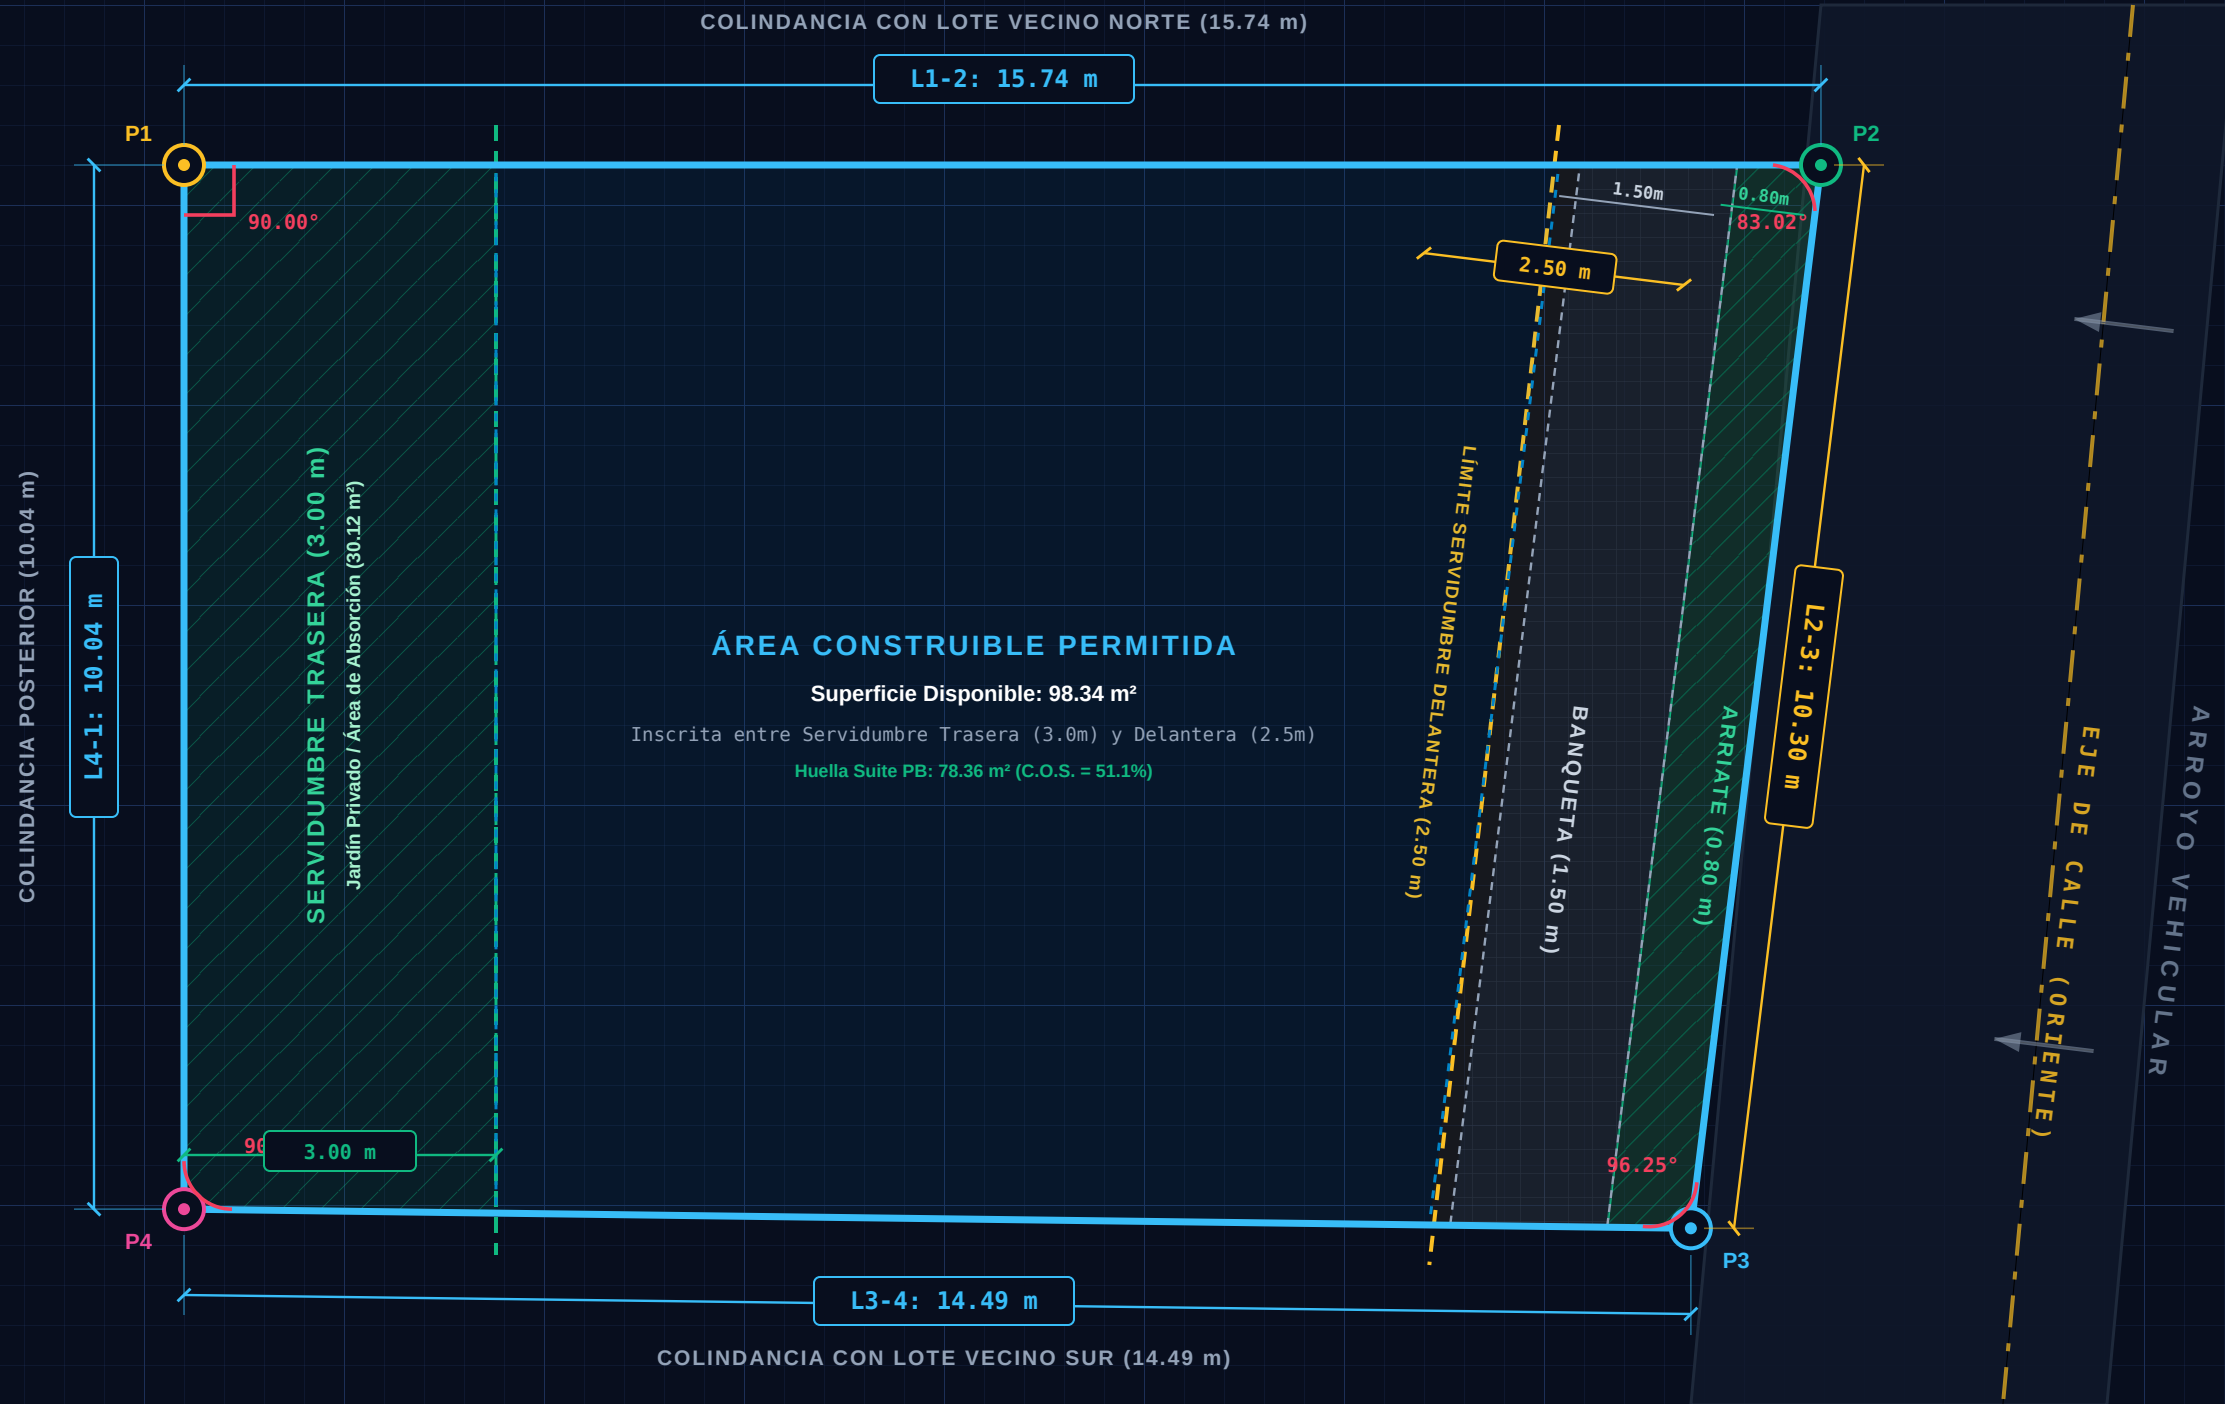


CUADRO DE CONSTRUCCIÓN (COORDENADAS EXACTAS)

EST	P.V.	RUMBO	DISTANCIA	COORD X (m)	COORD Y (m)
P1	P2	N 90°00'00" E	15.740 m	0.000	0.000
P2	P3	S 06°58'34" W	10.300 m	15.740	0.000
P3	P4	S 89°16'05" W	14.489 m	14.489	-10.224
P4	P1	N 00°00'00" E	10.040 m	0.000	-10.040
SUPERFICIE TOTAL:		153.19 m²	PERÍMETRO:	50.57 m	
ESQUINA RECTA:		P1 = 90.00° (Nor-Poniente)		DIAGONAL FRENTE:	ΔX = -1.25 m (6.98° al Este)

DESGLOSE DE SERVIDUMBRES Y SUPERFICIES

CONCEPTO	MEDIDA	ÁREA ESTIMADA
Servidumbre Trasera (Jardín)	3.00 m fondo	30.12 m²
Servidumbre Delantera Total	2.50 m (oblicua)	24.73 m²
↳ Arriate ajardinado (en 2.5m)	0.80 m	8.24 m²
↳ Banqueta peatonal (en 2.5m)	1.50 m	15.45 m²
↳ Margen interior de servidumbre	0.20 m	1.04 m²
ÁREA CONSTRUIBLE EN PB	8.97m a 10.22m	98.34 m²

CASA 235 • PLANO TOPOGRÁFICO Y SERVIDUMBRES

PROYECTO:
Levantamiento Geométrico, Servidumbres y Vialidad

UBICACIÓN:
Tlajomulco de Zúñiga, Jalisco

VIALIDAD:
Oriente / Este (Alineamiento L2-3)

SUPERFICIE:
153.19 m²

PERÍMETRO:
50.57 m

USO DE SUELO:
Habitacional (H3/H4)

ESCALA: 1:50 / Gráfica

ACOTACIONES: Metros (m)

FECHA: Septiembre 2026

CLAVE: TOP-01

SISTEMA: Cartesiano Ortogonal • Origen P1 (90.00°) • Servidumbre 2.50m (Banqueta 1.5m + Arriate 0.8m) • Inkscape 1.4

ESCALA GRÁFICA (METROS)

